



FIRST FLOOR

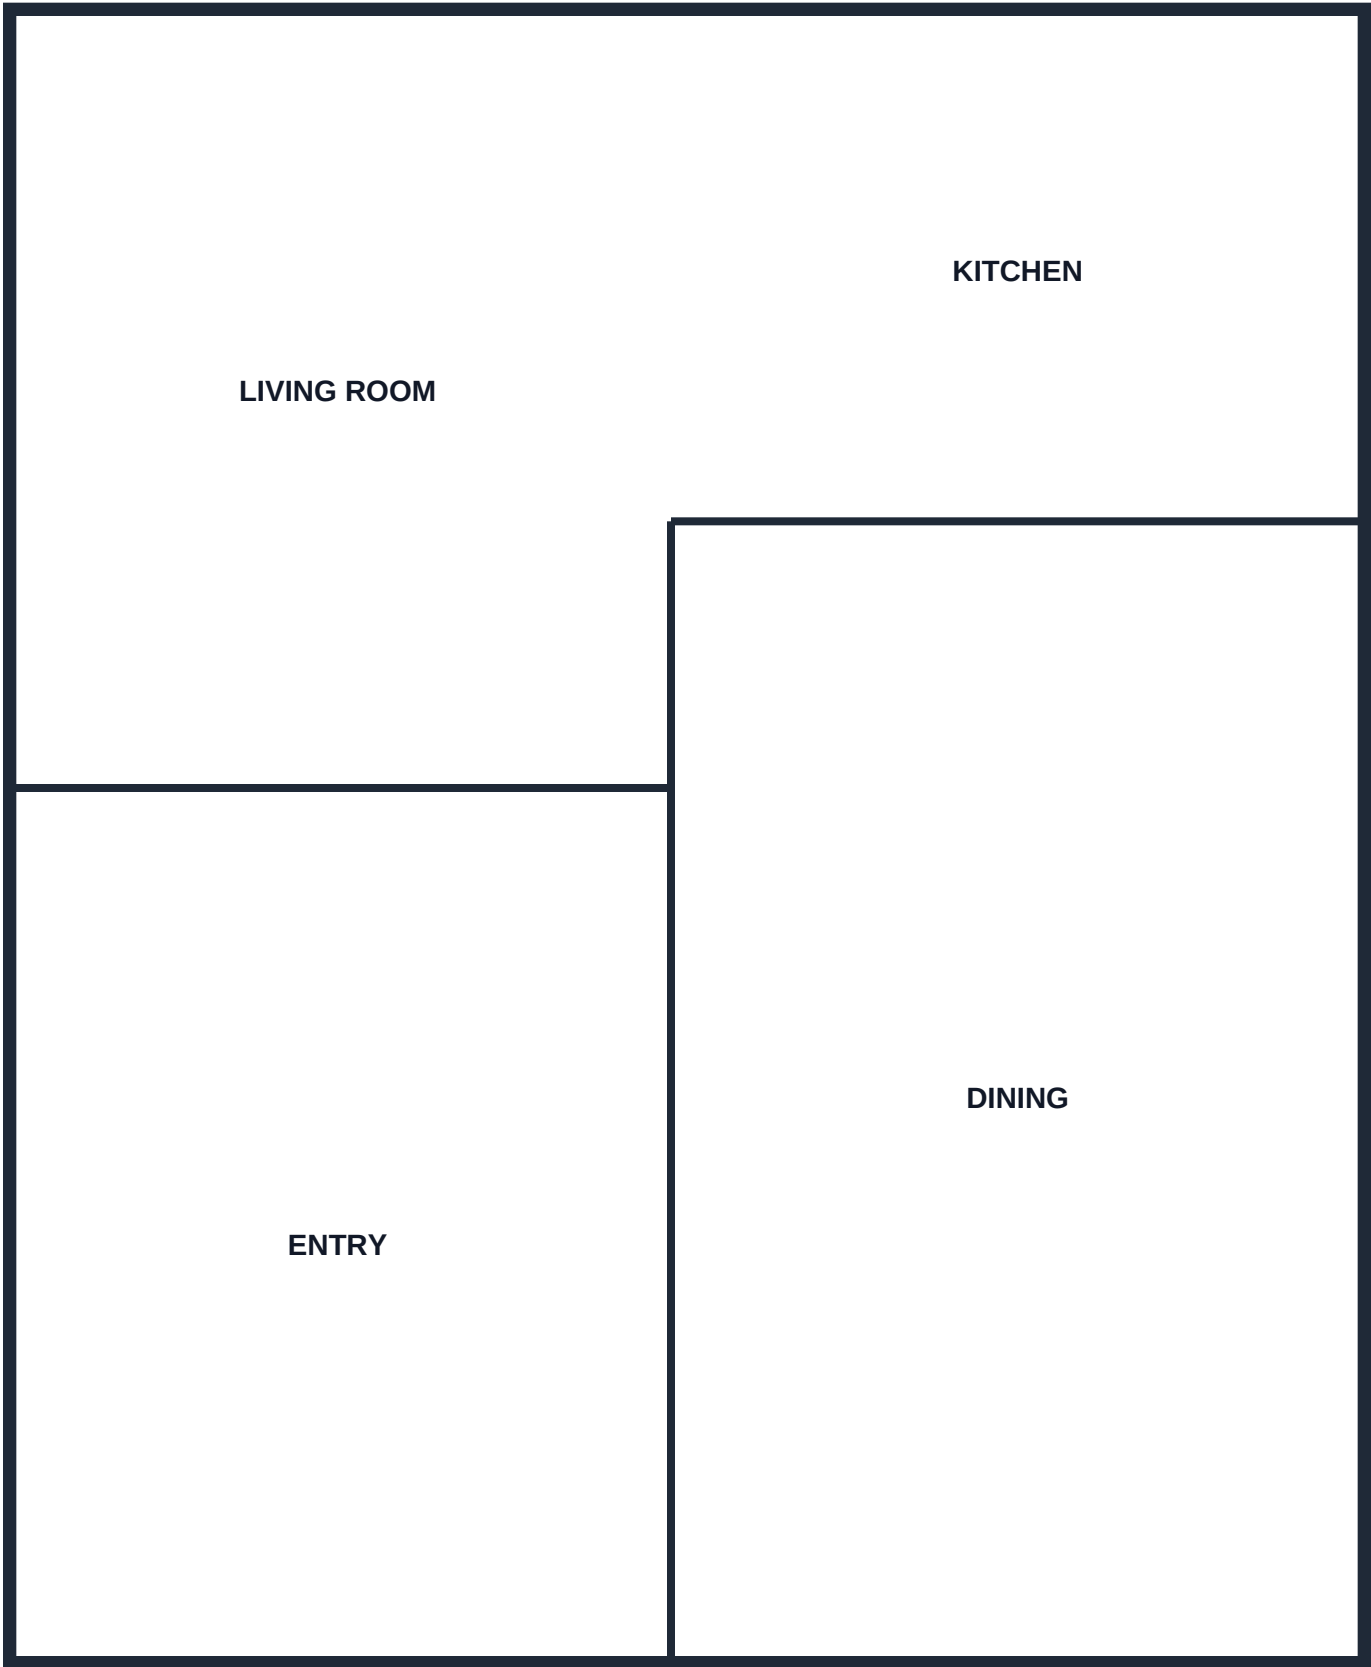

20 ft 0 in

SECOND FLOOR

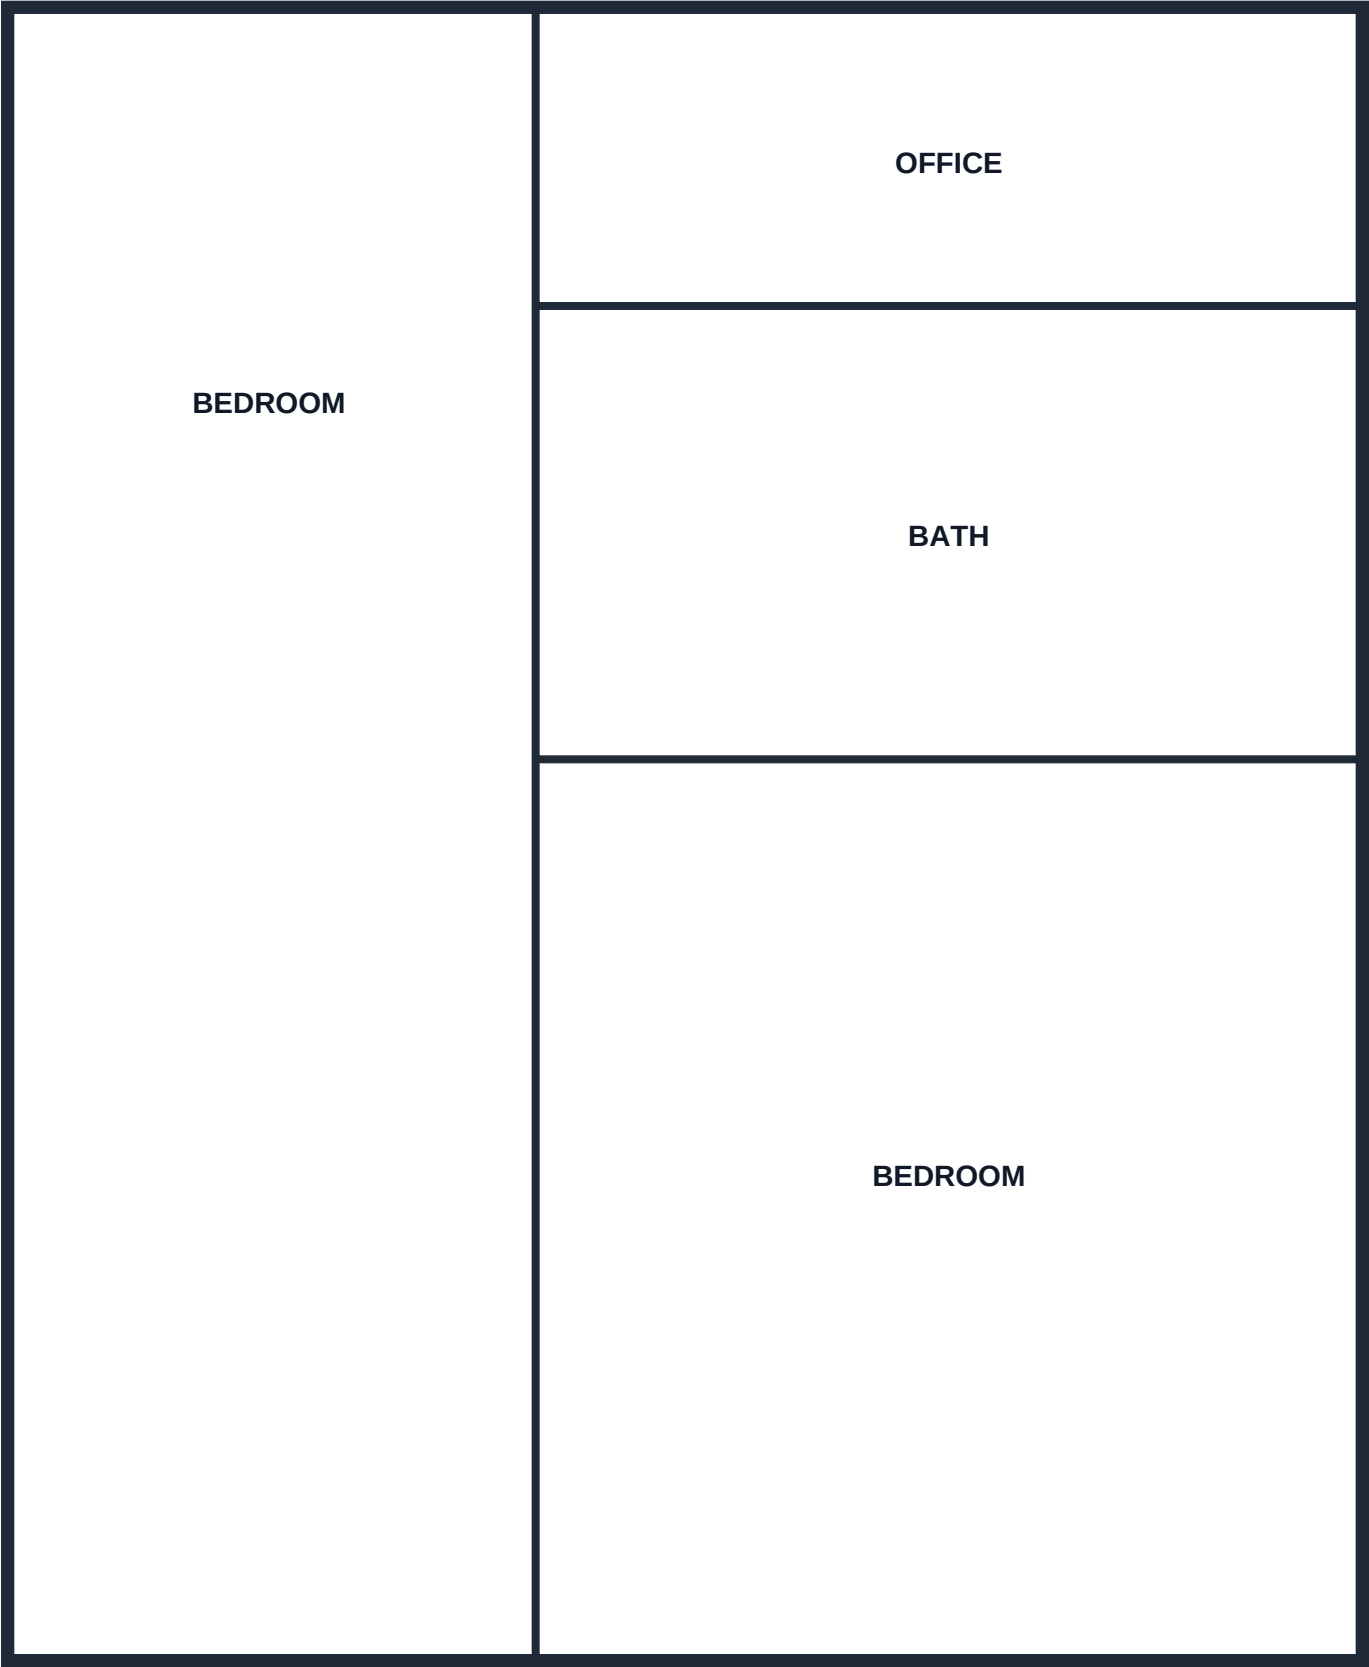

20 ft 0 in